

ТОВАРИЩЕСТВО С ОГРАНИЧЕННОЙ ОТВЕТСТВЕННОСТЬЮ



**Корректировка проекта «Реконструкция и
модернизация производственного комплекса
топливоподачи. Строительство дополнительного ввода
тракта топливоподачи ТОО «Экибастузская ГРЭС-1
имени Б. Нуржанова»»**

**РАБОЧАЯ ДОКУМЕНТАЦИЯ
ГЛАВНЫЙ КОРПУС.
КАБЕЛЬНОЕ ХОЗЯЙСТВО
ГАЛЕРЕИ ЛК 46/48 А,Б.
900585/2023/1-10-KX1.3**

**Павлодар
2026 г.**

ТОВАРИЩЕСТВО С ОГРАНИЧЕННОЙ ОТВЕТСТВЕННОСТЬЮ



**Корректировка проекта «Реконструкция и
модернизация производственного комплекса
топливоподачи. Строительство дополнительного ввода
тракта топливоподачи ТОО «Экибастузская ГРЭС-1
имени Б. Нуржанова»»**

**РАБОЧАЯ ДОКУМЕНТАЦИЯ
ГЛАВНЫЙ КОРПУС.
КАБЕЛЬНОЕ ХОЗЯЙСТВО
ГАЛЕРЕИ ЛК 46/48 А,Б.
900585/2023/1-10-КХ1.3**

Директор

Главный инженер

Главный инженер проекта



С.В. Быстров

А.П. Андреев

А.А. Демченко

Павлодар
2026 г.



ТОО «КУРЫЛЫС-ЖОБА СЕРВИС»

РАБОЧАЯ ДОКУМЕНТАЦИЯ

**Корректировка проекта «Реконструкция и
модернизация производства комплекса
топливоподачи. Строительство дополнительного
ввода тракта топливоподачи ТОО
«Экибастузская ГРЭС-1 имени Б.Нуржанова»**

**Главный корпус. Кабельное хозяйство галереи
ЛК 46-48 А,Б**

СИ-36-2023-10-КХ1.3



ТОО «КУРЫЛЫС-ЖОБА СЕРВИС»

РАБОЧАЯ ДОКУМЕНТАЦИЯ

**Корректировка проекта «Реконструкция и
модернизация производства комплекса
топливоподачи. Строительство дополнительного
ввода тракта топливоподачи ТОО
«Экибастузская ГРЭС-1 имени Б.Нуржанова»**

**Главный корпус. Кабельное хозяйство галереи
ЛК 46-48 А,Б**

СИ-36-2023-10-КХ1.3

Директор

Главный инженер

ГИП



В. Е. Санкин

А. И. Погудин

И.Н. Коршунов

г. Павлодар, 2026 г.

Согласовано

АСО

ТМО

ГТО

Инв. № подл.

Подпись и дата

Взам. инв. №

Лазаренко

Умурзакова

Нестеренко

Маковицкая

Ведомость рабочих чертежей основного комплекта

Лист	Наименование	Примечание
1	Общие данные	
2	План расположения кабельных конструкций в галерее ЛК №46А	
3	План расположения кабельных конструкций в галереях ЛК №46Б; №47А,Б и №48А	
4	План расположения кабельных конструкций в галерее ЛК №48Б	
5	План расположения кабельных конструкций в электрофильтре дл. №6	
6	План расположения кабельных конструкций в электрофильтре дл. №7	
7	План расположения кабельных конструкций в электрофильтре дл. №8	

Ведомость объемов строительных и монтажных работ

N п/п	Наименование	Ед. изм.	Кол.	Примечание
	Монтажные работы			
	Кабельные металлоконструкции	кг	3440,00	
	Кабельные конструкции (комплектные с ЛК)	кг	487,5	
	Отверстие с металлическим обрамлением размерами 350x500(н)	шт.	16	

Технические решения, принятые в рабочей документации, соответствуют требованиям экологических, санитарно-гигиенических, противопожарных и других норм, действующих на территории Республики Казахстан и обеспечивают безопасную для жизни и здоровья людей эксплуатацию объекта при соблюдении предусмотренных рабочими чертежами

Главный инженер проекта _____ И.Н.Коршунов

Ведомость ссылочных и прилагаемых документов


Обозначение	Наименование	Примечание
	Ссылочные документы	
ПУЭ РК	Правила устройства электроустановок	
СИ-36-2023-10-ЭМ2.3	Главный корпус. Блочные конвейера ЛК46-ЛК48 А,Б. Электрооборудование	
	Прилагаемые документы	
СИ-36-2023-10-КХ1.3.СО	Спецификация оборудования, изделий и материалов	

Общие указания

Настоящий проект разработан на основе договора СИ-36-2023 от 01.08.23г.
В проекте выполнен план расположения кабельных конструкций в галереях ЛК №46-48А,Б, а также в помещениях электрофильтров блоков №6...№8
Для прокладки кабеля используются кабельные лотки лестничного типа, монтаж которых осуществляется на закладных деталях кабельных металлоконструкций. Кабельные конструкции крепить с шагом 1 м. В местах проходов кабелей через стены для обеспечения пожарной безопасности установить огнестойкие плиты ДР. Для обеспечения предела огнестойкости 90 минут глубина заделки из плит должна быть не менее 200мм, т.е. необходимо установить четыре куска плиты ДР одну за другой. Для лучшей герметизации проходов нанести слой огнестойкого герметика DS толщиной не менее 3мм на все элементы заделки.
Также в проекте предусматривается монтаж кабельных лотков вдоль ставов ЛК№46-48 А,Б. Данные кабельные лотки монтируются по месту и поставляются комплектно с ЛК (см. ведомость строительных и монтажных работ)
Данный рабочий проект рассматривать совместно с проектом СИ-36-2023-10-ЭМ2.3
Монтаж выполнить в соответствии с ПУЭ РК и СНиП РК 4.04.10-2002 "Электротехнические устройства"


						СИ-36-2023-10-КХ1.3			
1		Изм.	05-26	К.С.	01.26	"Реконструкция и модернизация производственного комплекса топливоподачи. Строительство дополнительного ввода тракта топливоподачи ТОО "Экибастузская ГРЭС-1 им. Б.Нуржанова"			
Изм.	Кол.уч.	Лист	Идок	Подп.	Дата				
						Главный корпус. Кабельное хозяйство галерей ЛК 46-48 А,Б	Стадия	Лист	Листов
ГИП	Коршунов			М.С.	08.24		РД	1	7
Нач.отд.	Мызовский			К.С.	08.24	Общие данные	ТОО "Курылыс-жоба сервис"		
Разраб.	Амренова			А.С.	08.24				
Н.контр	Мызовский			К.С.	08.24				

План на отм. +35,100

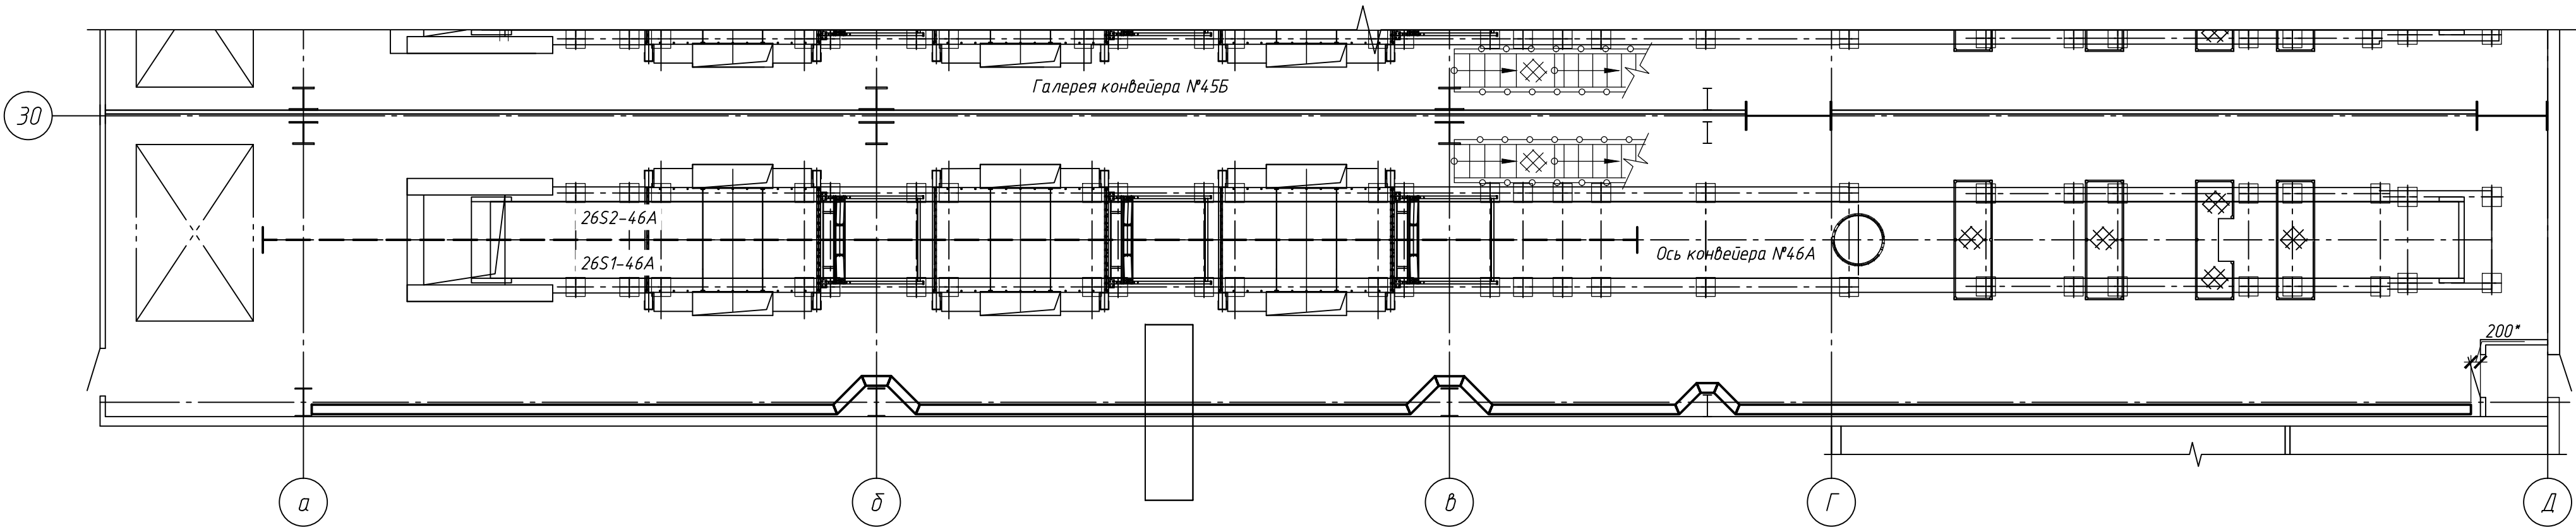

Спецификация

Поз.	Обозначение	Наименование	Кол.	Масса ед., кг	Приме- чание
1		Лоток кабельный НЛ-20П1.87 УЗ	52	4,5	
2		Полка кабельная К1161Ц УТ1,5	110	0,21	
3		Стойка кабельная К1150 Ц УТ1,5	55	0,69	
4		Скоба К1157 УЗ	110	0,14	
5		Прижим НЛ-ПР	220	0,03	
6		Анкерный болт с гайкой 8х120	220	0,007	

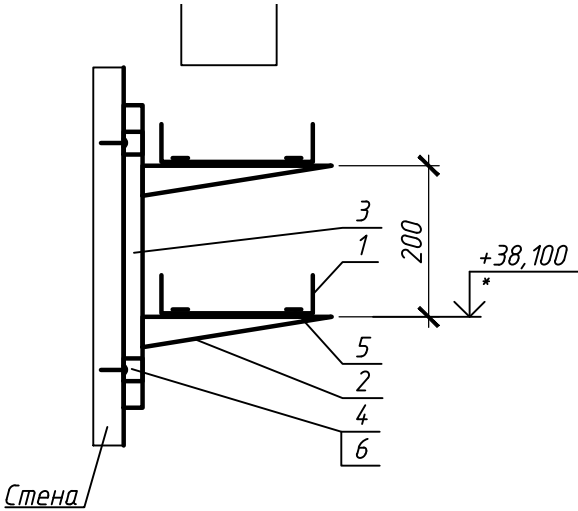


* Размеры, отметка даны для справок и уточняются при монтаже
Монтаж выполнить согласно ПУЭ РК

							СИ-36-2023-10-КХ1.3		
							"Реконструкция и модернизация производственного комплекса топливopодачи. Строительство дополнительного ввода тракта топливopодачи ТОО "Экибастузская ГРЭС-1 им. Б.Нуржанова"		
Изм.	Колуч.	Лист	Ндок	Подп.	Дата		Главный корпус. Кабельное хозяйство галерей ЛК 46-48 А,Б		
							РД	2	
Проверил	Мызовский				08.24		План расположения кабельных конструкций в галерее ЛК №46А		
Разраб.	Амренова				08.24				
Н.контр	Мызовский				08.24				
							ТОО "Курылыс-жоба сервис"		


Инв. № подл. Подпись и дата Взам. инв. №

План на отм. +35,100

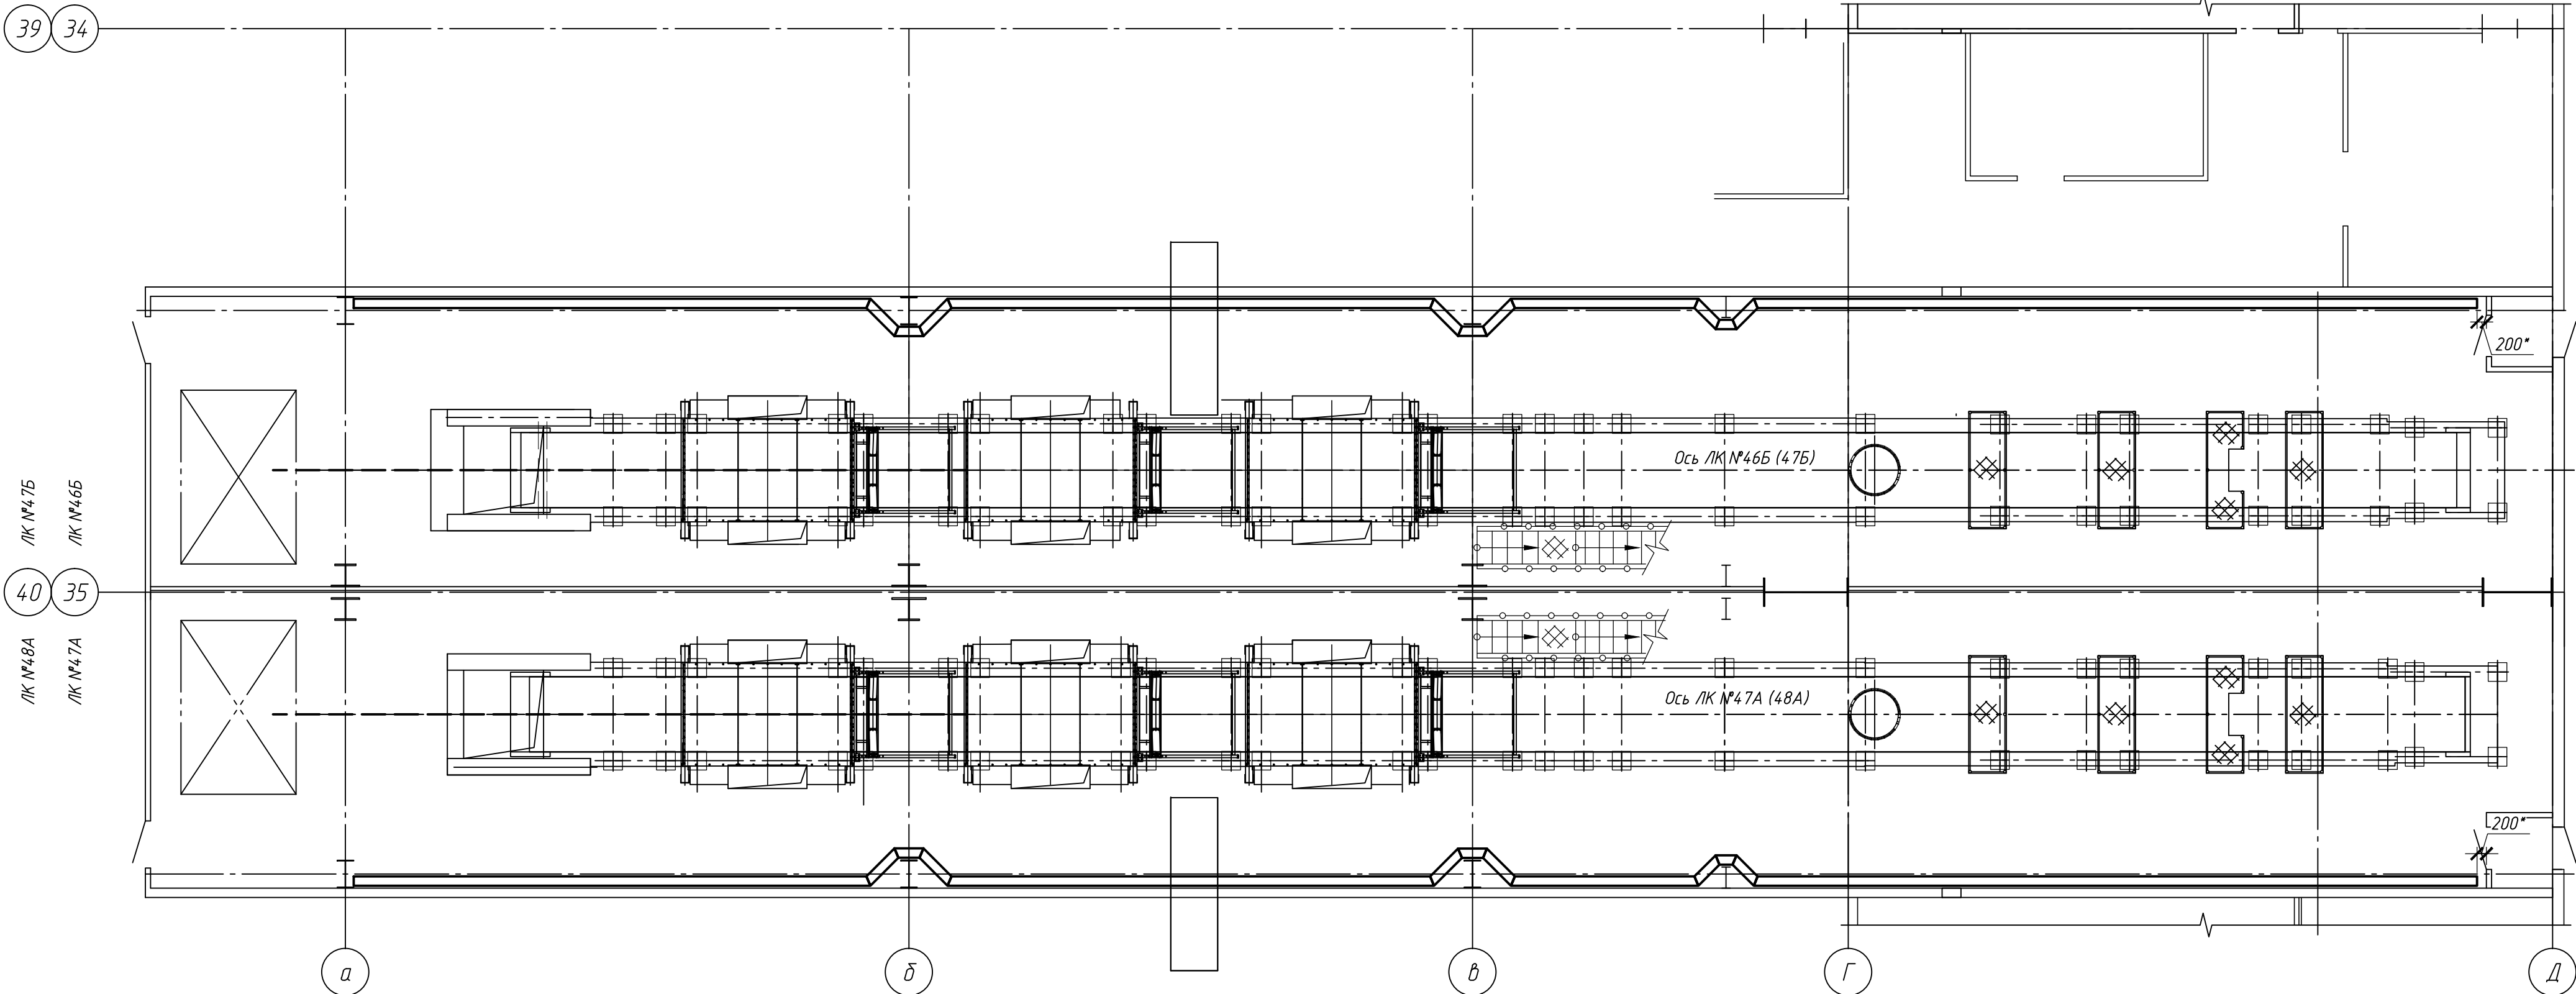

Спецификация


Поз.	Обозначение	Наименование	Кол.	Масса ед., кг	Приме- чание
1		Лоток кабельный НЛ-20П1.87 УЗ	208	4,5	
2		Полка кабельная К1161Ц УТ1,5	440	0,21	
3		Стойка кабельная К1150 Ц УТ1.5	220	0,69	
4		Скоба К1157 УЗ	440	0,14	
5		Прижим НЛ-ПР	880	0,03	
6		Анкерный болт с гайкой 8х120	880	0,007	

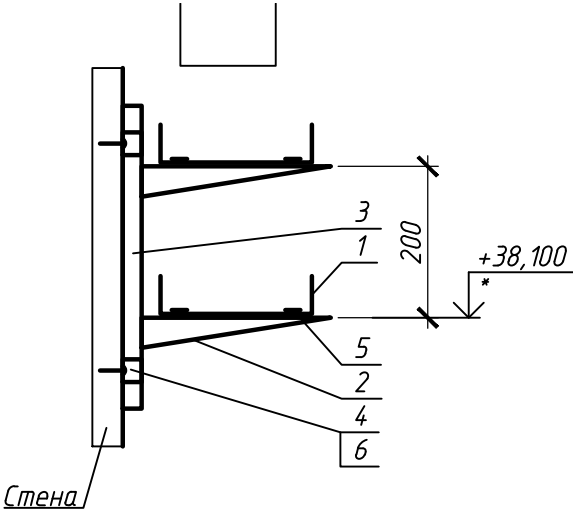

* Размеры, отметка даны для справок и уточняются при монтаже
Монтаж выполнить согласно ПУЭ РК


						СИ-36-2023-10-КХ1.3		
						"Реконструкция и модернизация производственного комплекса топливopодачи. Строительство дополнительного ввода тракта топливopодачи ТОО "Экибастузская ГРЭС-1 им. Б.Нуржанаова"		
Изм.	Колуч.	Лист	Ндок	Подп.	Дата	Главный корпус. Кабельное хозяйство галерей ЛК 46-48 А,Б	Стадия	Лист
							РД	3
Проверил	Мызовский				08.24	План расположения кабельных конструкций в галереях ЛК №46Б; №47А,Б и №48А	ТОО "Курылыс-жоба сервис"	
Разраб.	Амренова				08.24			
Н.контр	Мызовский				08.24			

План на отм. +35,100

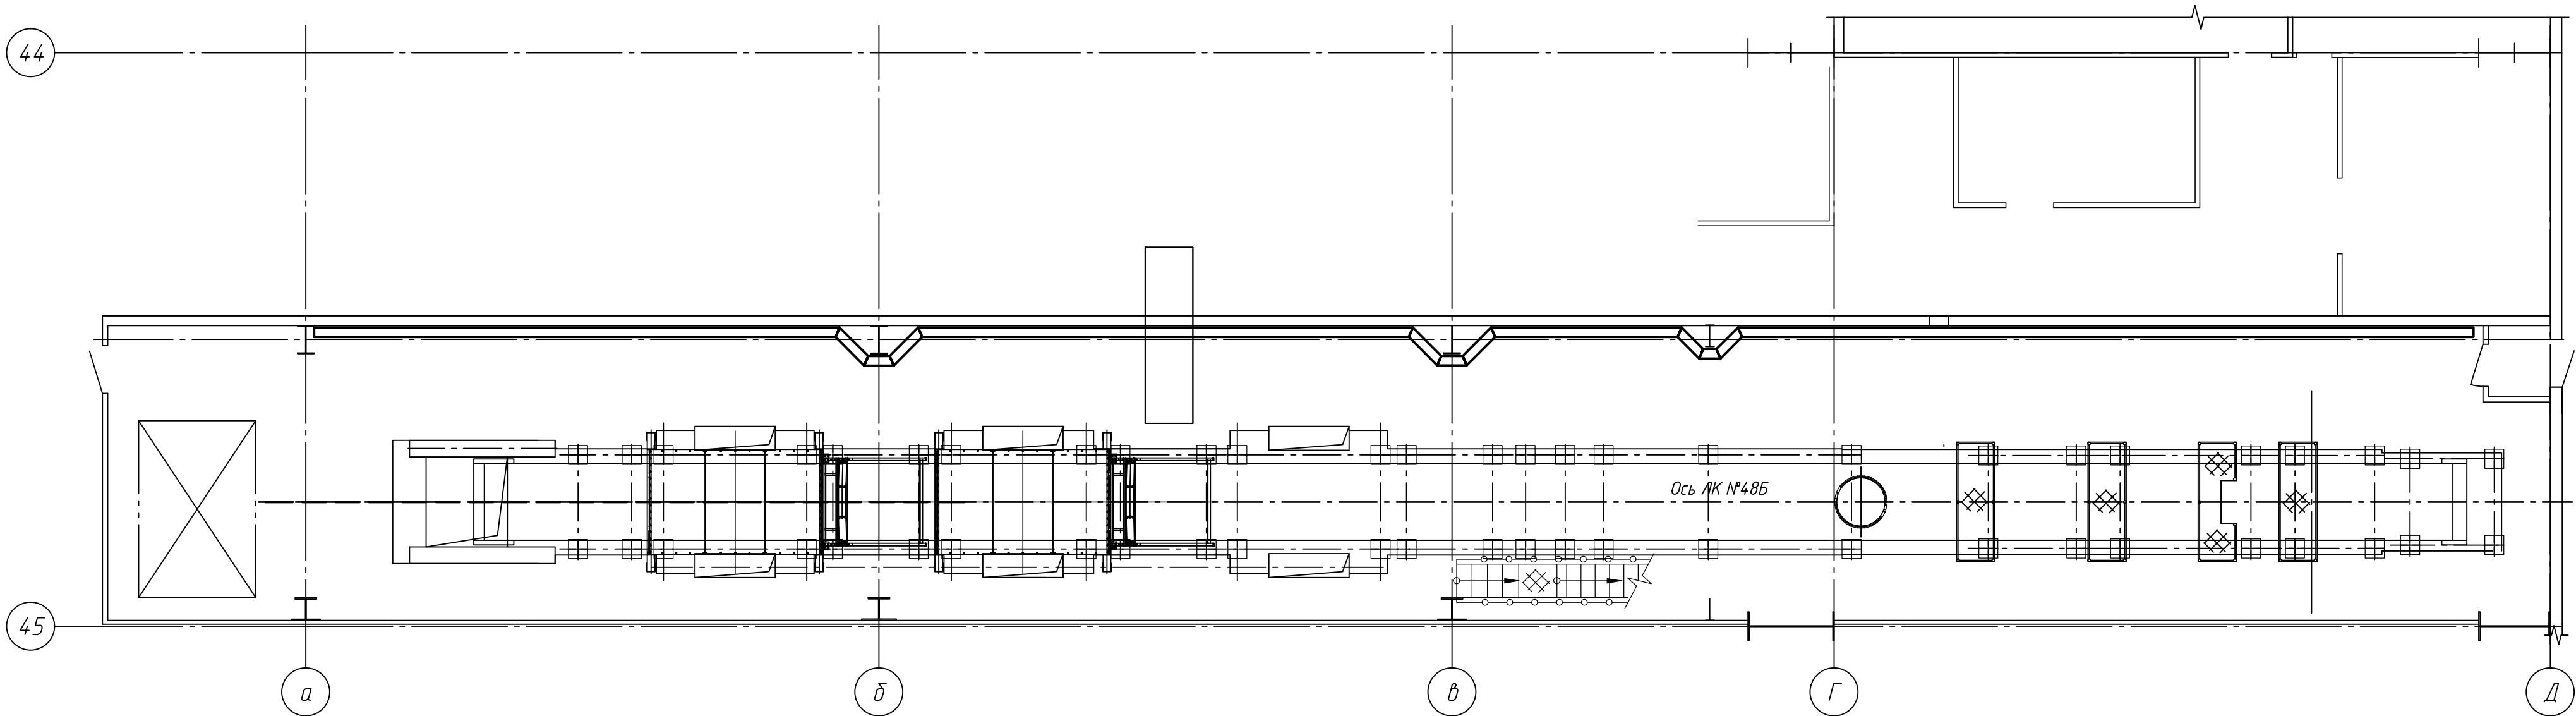


Спецификация

Инф. N подл.	Подпись и дата	Взам. инф. N	Поз.	Обозначение	Наименование	Кол.	Масса ед., кг	Приме- чание
			1		Лоток кабельный НЛ-20П1.87 УЗ	52	4,5	
			2		Полка кабельная К1161Ц УТ1,5	110	0,21	
			3		Стойка кабельная К1150 Ц УТ1,5	55	0,69	
			4		Скоба К1157 УЗ	110	0,14	
			5		Прижим НЛ-ПР	220	0,03	
			6		Анкерный болт с гайкой 8х120	220	0,007	

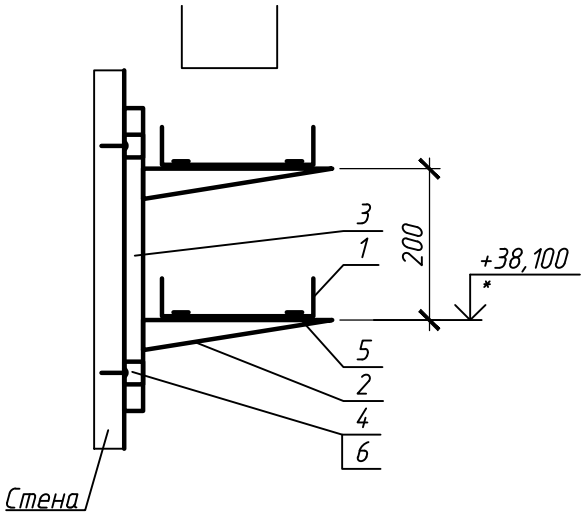


* Размеры, отметка даны для справок и уточняются при монтаже
Монтаж выполнить согласно ПУЭ РК

						СИ-36-2023-10-КХ1.3		
						"Реконструкция и модернизация производственного комплекса топливopодачи. Строительство дополнительного ввода тракта топливopодачи ТОО "Экибастузская ГРЭС-1 им. Б.Нуржанова"		
Изм.	Колуч.	Лист.	Ндок	Подп.	Дата	Главный корпус. Кабельное хозяйство галерей ЛК 46-48 А,Б		Стадия
								Лист
								Листов
Проверил	Мызовский				08.24	План расположения кабельных конструкций в галерее ЛК №48Б		ТОО "Курылыс-жоба сервис"
Разраб.	Амренова				08.24			
Н.контр	Мызовский				08.24			

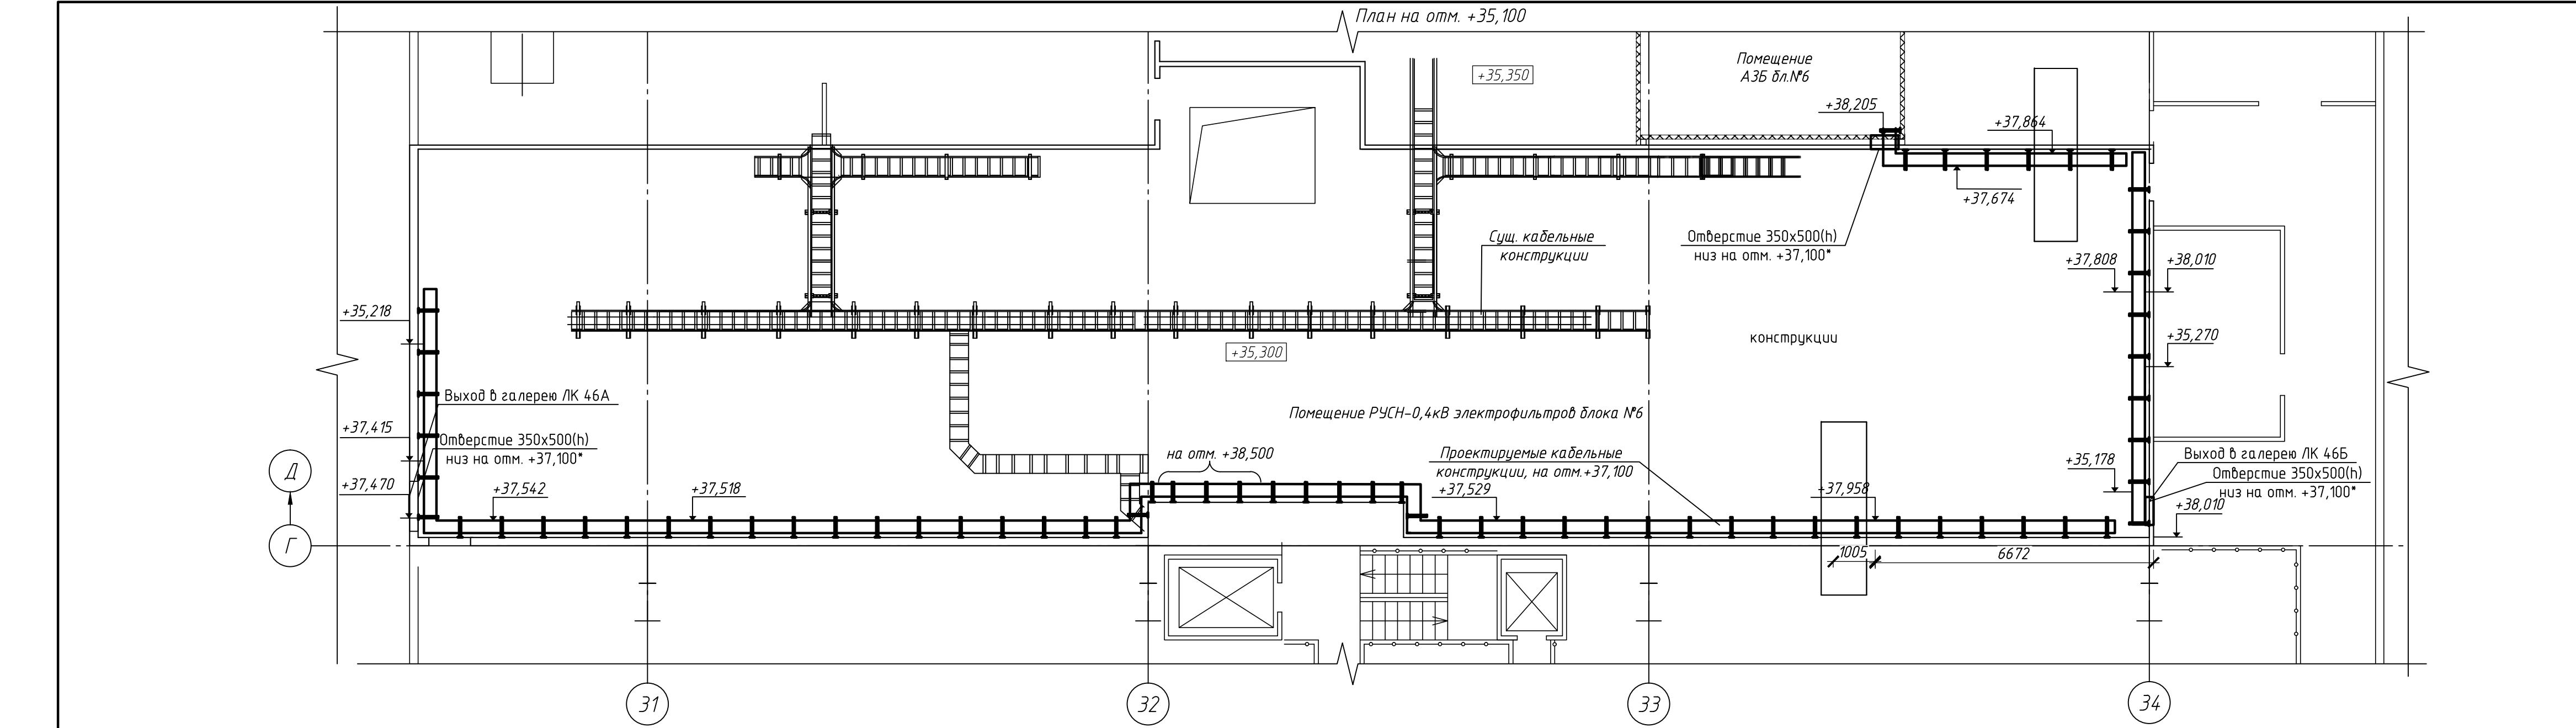



Спецификация

Поз.	Обозначение	Наименование	Кол.	Масса ед., кг	Приме- чание
1		Лоток кабельный НЛ-30П187 УТ2,5	72	5,8	
2		Полка кабельная К1162 Ц УТ1,5	142	0,47	
3		Стойка кабельная К1150 Ц УТ1,5	71	0,69	
4		Скоба К1157 УЗ	142	0,14	
5		Прижим НЛ-ПР	284	0,03	
6		Анкерный болт с гайкой 8x120	24	0,007	
7	ГОСТ 2590-2006	Прокат стальной горячекатаный круглый Ø12, м	35,4	0,888	

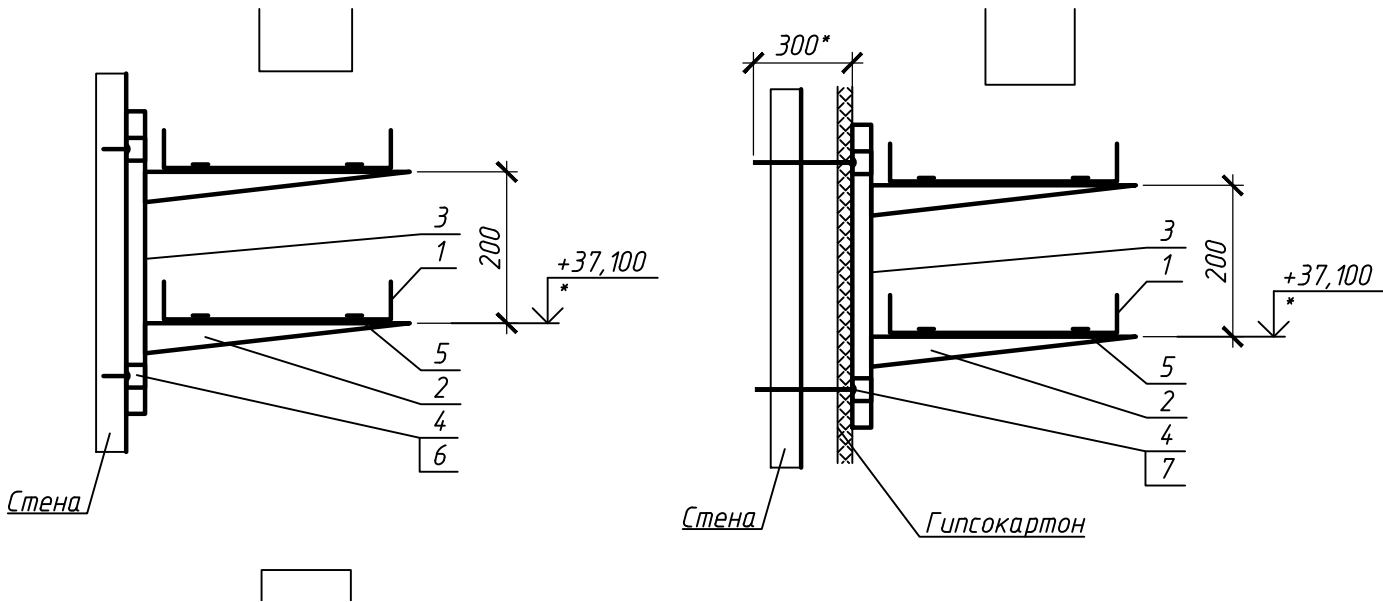

- * Размеры, отметка даны для справок и уточняются при монтаже
1. Монтаж выполнить согласно ПУЭ РК.
 2. Прокладка кабельных конструкций приведена в соответствии с документами, выданными заказчиком

						СИ-36-2023-10-КХ1.3				
1		Изм.	05-26	К.С.	01.26	"Реконструкция и модернизация производственного комплекса топливopодачи. Строительство дополнительного ввода тракта топливopодачи ТОО "Экибастузская ГРЭС-1 им. Б.Нуржанова"				
Изм.	Колуч.	Лист.	Док.	Подп.	Дата					
						Главный корпус. Кабельное хозяйство галерей ЛК 46-48 А,Б		Стадия	Лист	Листов
								РД	5	
Проверил	Мызовский				08.24	План расположения кабельных конструкций в электрофильтре блока №6			ТОО "Курылыс-жоба сервис"	
Разраб.	Амренова				08.24					
Н.контр	Мызовский				08.24					

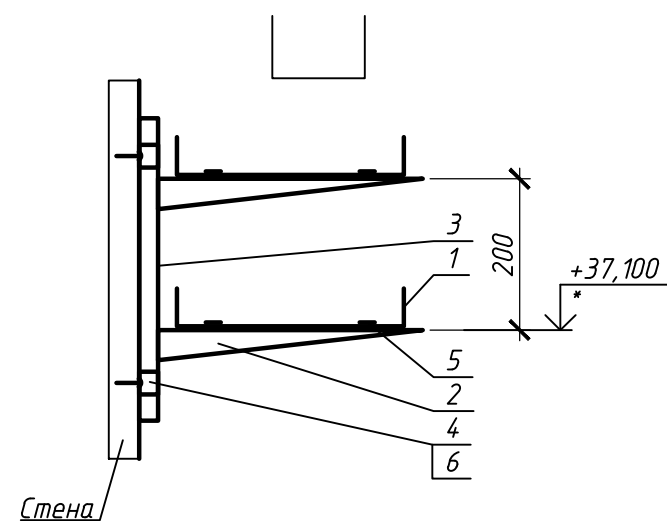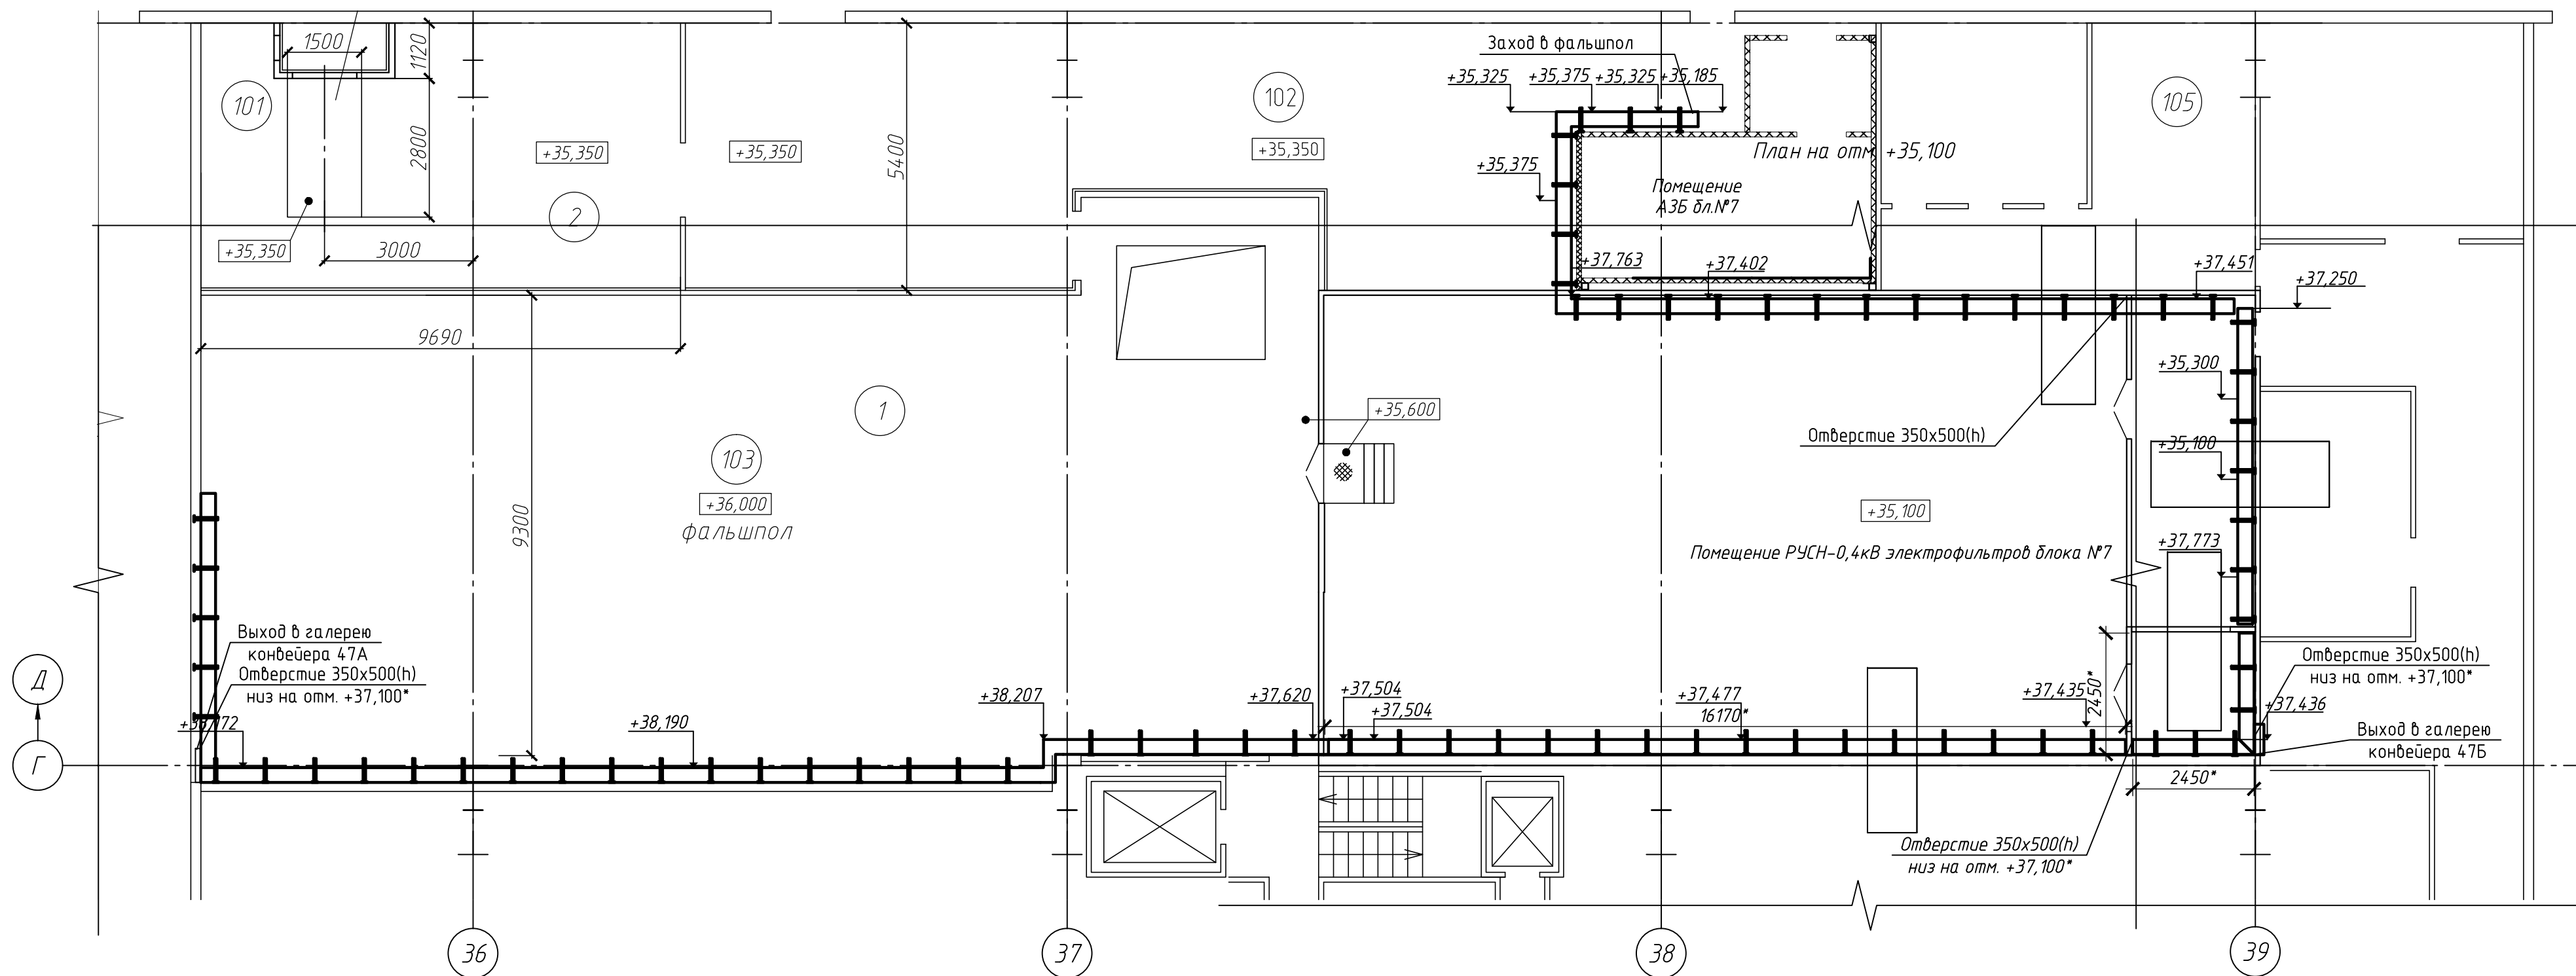


Спецификация

Поз.	Обозначение	Наименование	Кол.	Масса ед., кг	Приме- чание
1		Лоток кабельный НЛ-30П187 УТ2.5, шт.	46	5,8	
2		Полка кабельная К1162 Ц УТ1,5	90	0,47	
3		Стойка кабельная К1150 Ц УТ1,5	45	0,69	
4		Скоба К1157 УЗ	90	0,14	
5		Прижим НЛ-ПР	180	0,03	
6		Анкерный болт с гайкой 8х120	90	0,007	

- * Размеры, отметка даны для справок и уточняются при монтаже
1. Монтаж выполнить согласно ПУЭ РК.
 2. Прокладка кабельных конструкций приведена в соответствии с документами, выданными заказчиком

						СИ-36-2023-10-КХ1.3		
						"Реконструкция и модернизация производственного комплекса топливopодачи. Строительство дополнительного ввода тракта топливopодачи ТОО "Экибастузская ГРЭС-1 им. Б.Нуржанова"		
1		Изм.	05-26	К.С.	01.26	Главный корпус. Кабельное хозяйство галерей ЛК 46-48 А,Б		
Изм.	Колуч.	Лист	Идок	Подп.	Дата			
						Стадия	Лист	Листов
						РД	6	
Проверил	Мызовский			К.С.	08.24	План расположения кабельных конструкций в электрофильтре блока №7		
Разраб.	Амренова			А.М.	08.24			
Н.контр	Мызовский			К.С.	08.24			
						ТОО "Курылыс-жоба сервис"		

Взам. инв. N	
Подпись и дата	
Инв. N подл.	

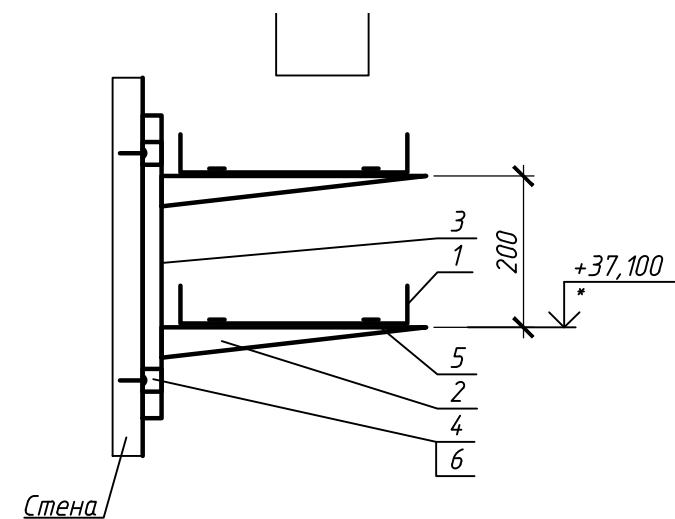

* Размеры, отметка даны для справок и уточняются при монтаже

						СИ-36-2023-10-КХ1.3			
						"Реконструкция и модернизация производственного комплекса топливopодачи. Строительство дополнительного ввода тракта топливopодачи ТОО "Экидастузская ГРЭС-1 им. Б.Нуржанова"			
Изм.	Колуч.	Лист	Идок	Подп.	Дата	Главный корпус. Кабельное хозяйство галерей ЛК 46-48 А,Б	Стадия	Лист	Листов
							РД	7	
Проверил	Мызовский				08.24	План расположения кабельных конструкций в электрофильтре блока №8	ТОО "Курылыс-жоба сервис"		
Разраб.	Амренова				08.24				
Н.контр	Мызовский				08.24				

Инв. N подл.	Подпись и дата	Взам. инв. N

[illegible]

						СИ-36-2023-10-KX1.3.CO					
						"Реконструкция и модернизация производственного комплекса топливopодачи. Строительство дополнительного ввода тракта топливopодачи ТОО "Экибастузская ГРЭС-1 им.Б.Нуржанова"					
Изм.	Колуч.	Лист	Ндок.	Подпись	Дата						
						Главный корпус. Кабельное хозяйство галерей ЛК 46-48А,Б			Стадия	Лист	Листов
									РД		1
ГИП		Коршунов			08.24	Спецификация оборудования, изделий и материалов			ТОО "Курылыс-жоба сервис"		
На ч.отд.		Мызовский			08.24						
Разраб.		Амренова			08.24						
Н.контр.		Мызовский			08.24						