
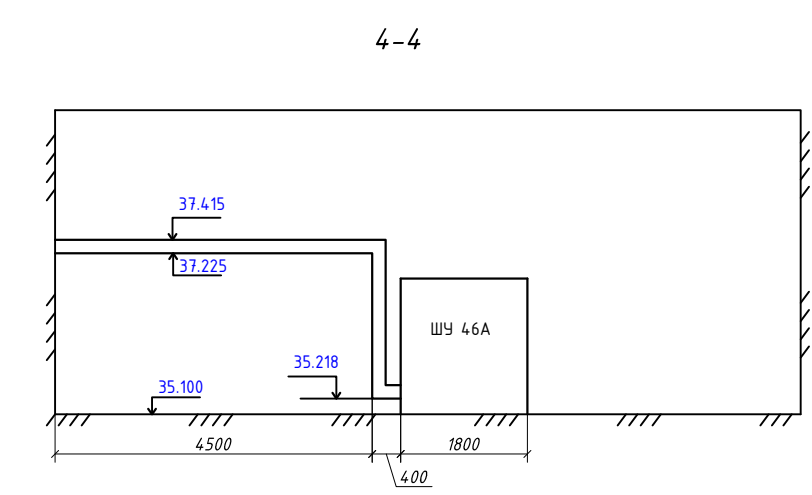
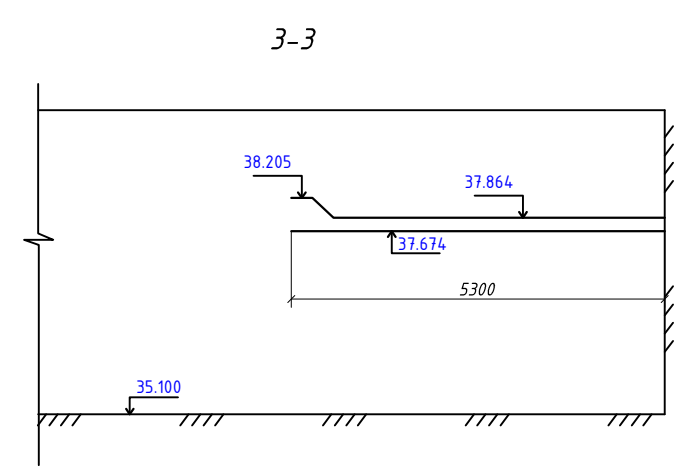
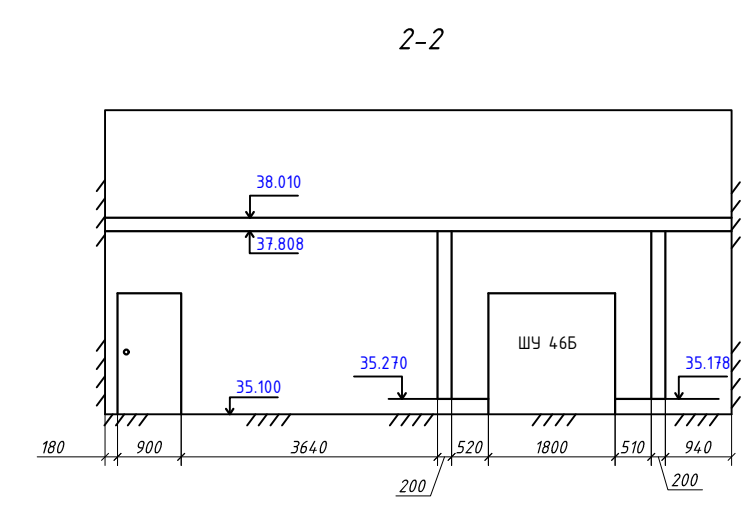


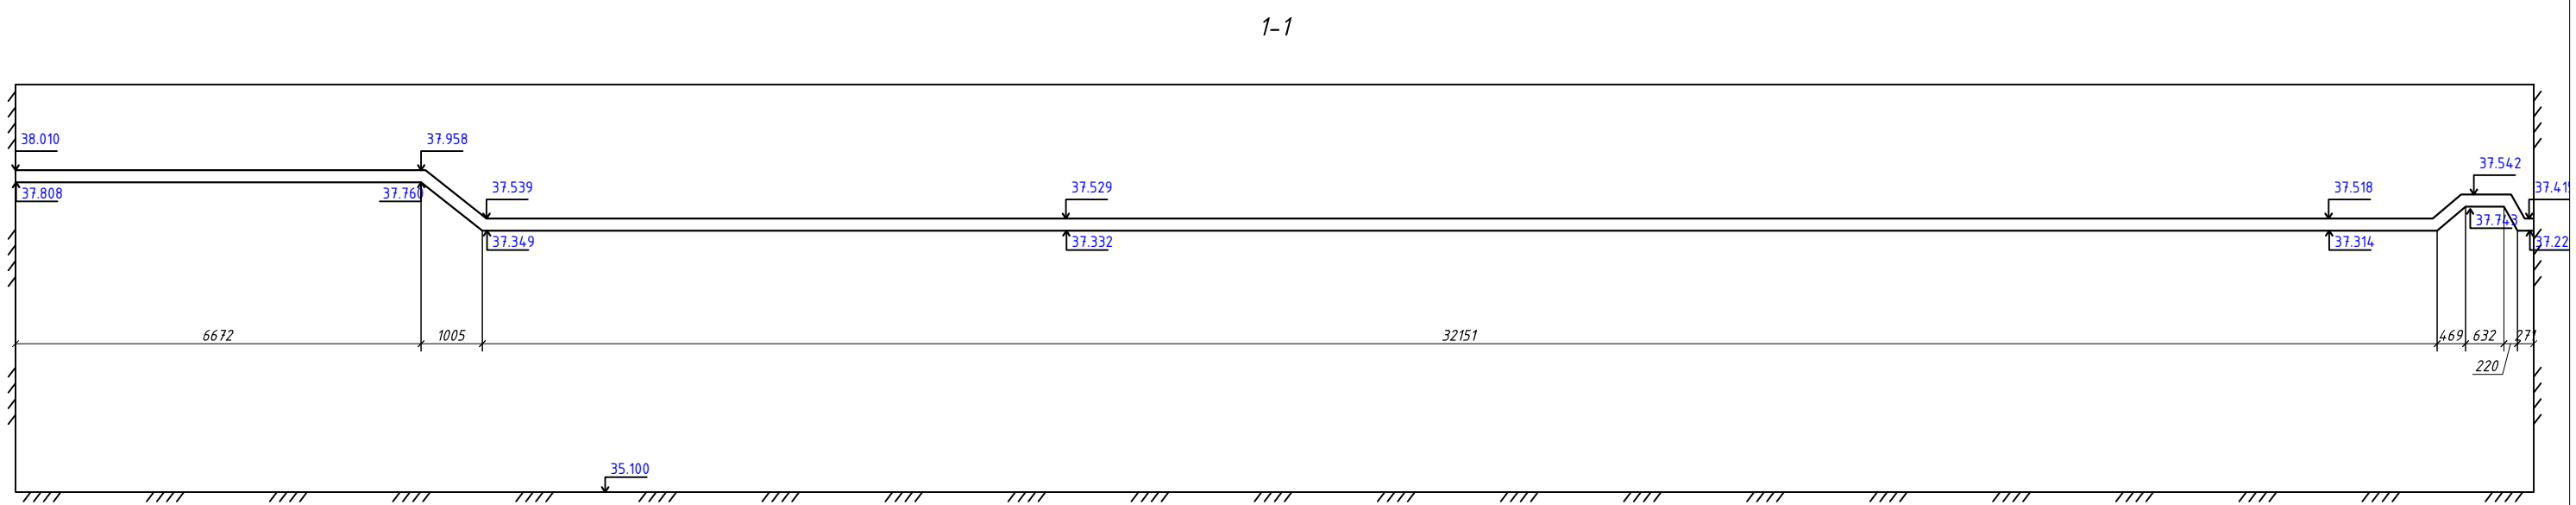

				СИ-36-2023-10- КХ 1.3		
				"Реконструкция и модернизация производственного комплекса топливopодачи. Строительство дополнительного ввода тракта топливopодачи ТОО "Экибастузская ГРЭС -1 им. Б.Нуржанова"		
Должность	Ф.И.О.	Подпись	Дата	Главный корпус. Кабельное хозяйство галерей ЛК 46-48 А,Б	Лист	Листов
					2	2
				Съемка расположения кабельных конструкций ЛК 46. Разрезы		