


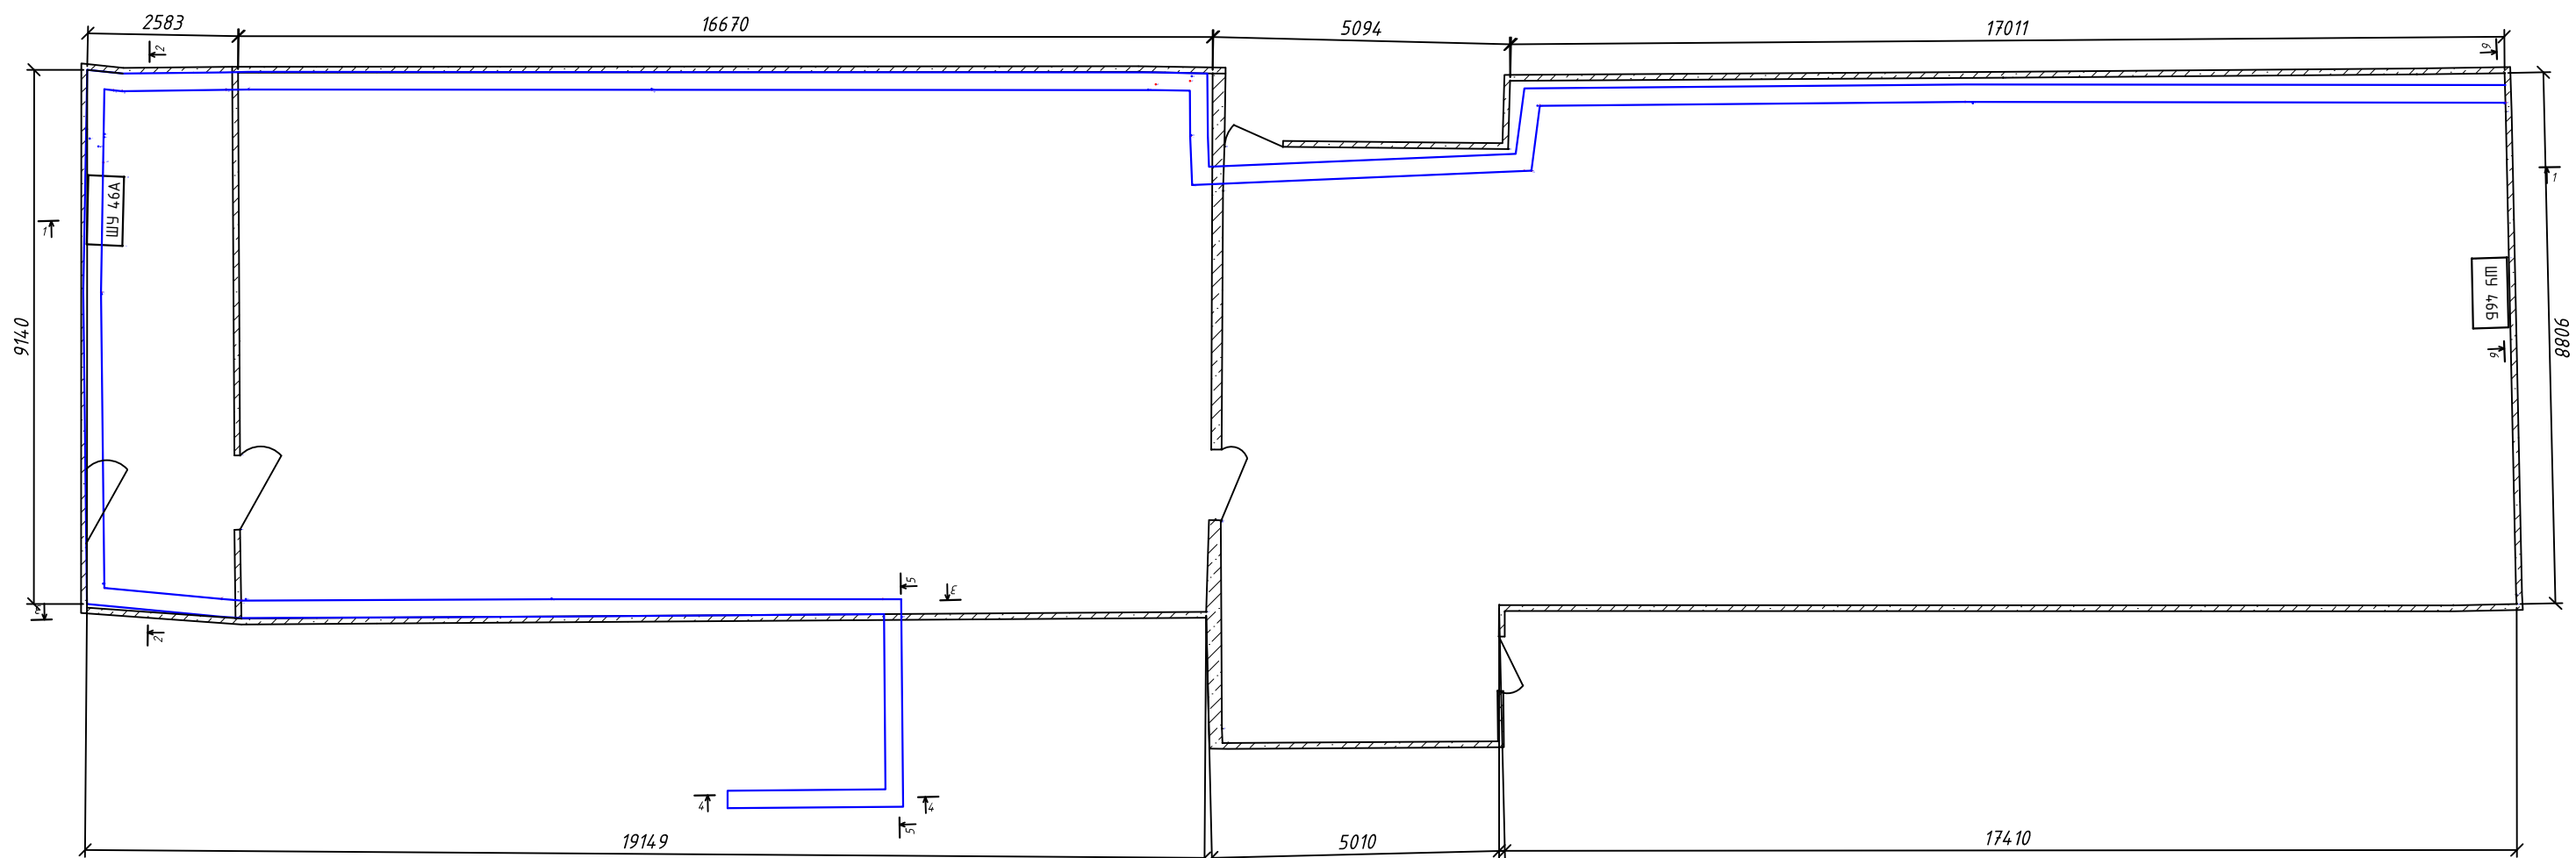

Примечание:

— — Кабельный лоток

Отметка пола +35,100

				СИ-36-2023-10- КХ 1.3		
				"Реконструкция и модернизация производственного комплекса топливоподачи. Строительство дополнительного ввода тракта топливоподачи ТОО "Экибастузская ГРЭС -1 им. Б.Нуржанова"		
Должность	Ф.И.О.	Подпись	Дата	Главный корпус. Кабельное хозяйство галерей ЛК 46-48 А,Б		
					Лист	Листов
					1	2
				Съемка расположения кабельных конструкций ЛК 47. План		